Loreto Salazar Salina


ARCHITECT · SELECTED WORKS

Rural and territorial architecture across Chile, from Patagonia to the Atacama Desert. Design rooted in landscape, climate and local materials, carried through surveys, permits and construction.

refugionomada.cl · lsalazarsalina@gmail.com · +56 9 7952 5044





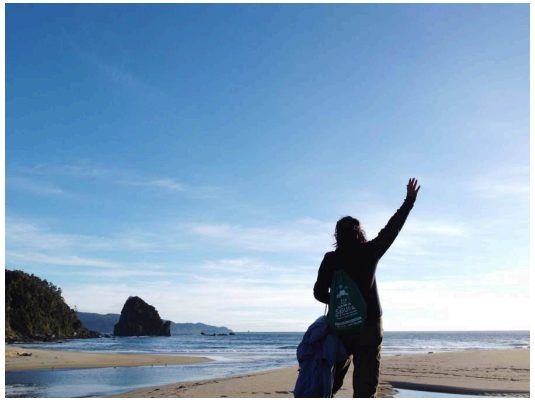

About


Architect, mapping territories.

I'm Loreto Salazar Salina, a licensed Chilean architect born in Temuco, in the south of Chile. For more than ten years I have worked on rural projects, building permits and territorial planning, from the Atacama Desert to Cape Horn. My practice was born from the land itself: unpaved roads, riverbanks, communities that build with what they have.

I understand architecture as an act of listening before designing: a process that moves with people and landscapes.

In 2026 I joined the crew of the sailing boat Silver Harmony: 2,654 nautical miles, including an 18-day crossing of the North Atlantic. The sea taught me about small spaces, weather, and working as a team with very little. Now I am in Thailand, and from the road I keep designing.

REG. N° 300833 · RURAL ARCHITECTURE · PERMITS · BIOCONSTRUCTION

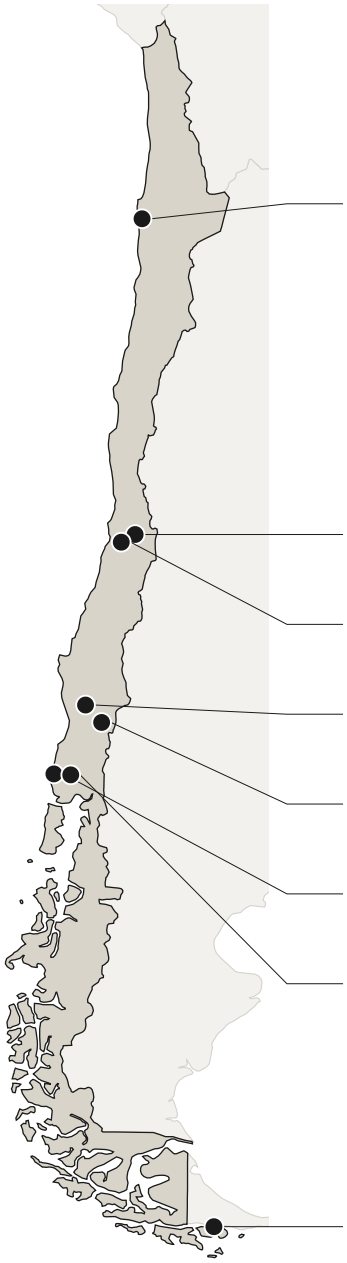

Antofagasta

Santiago
Retail permits · Site studies · University

Melipilla
Municipality · Own practice: Lumbreras, Culiprán, Mausoleum

Temuco
Hometown


Pucón
Quincho Pucón · Own practice

Manquemapu
Refugio Leucotón · Osorno, Los Lagos Region · Own practice

Purranque
Own practice

Puerto Williams
Subantarctic Center (Salfa) · Navarino tiny houses

How I got here · 2026

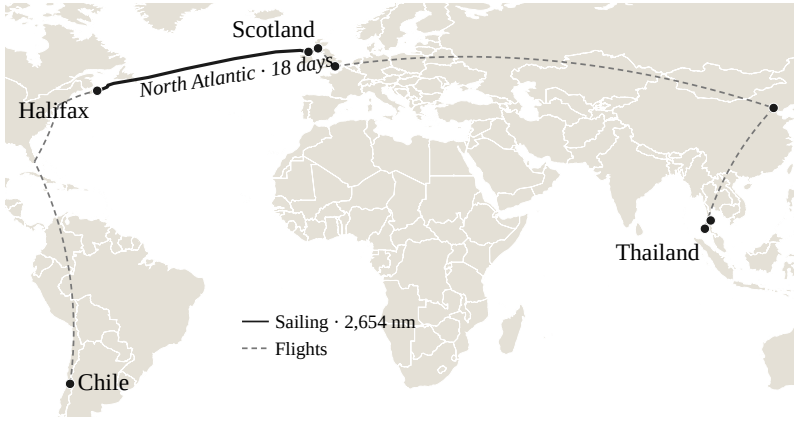

Where I've Worked


Chile 2014–2026 · Thailand 2026

From the Atacama Desert to Cape Horn: more than ten years of work across Chile, with very different climates, materials and building cultures.

In 2026 I crossed the North Atlantic as crew on the sailing boat Silver Harmony (2,654 nautical miles) and then flew to Thailand, where I am now.

TERRITORY · CLIMATE · LOCAL BUILDING



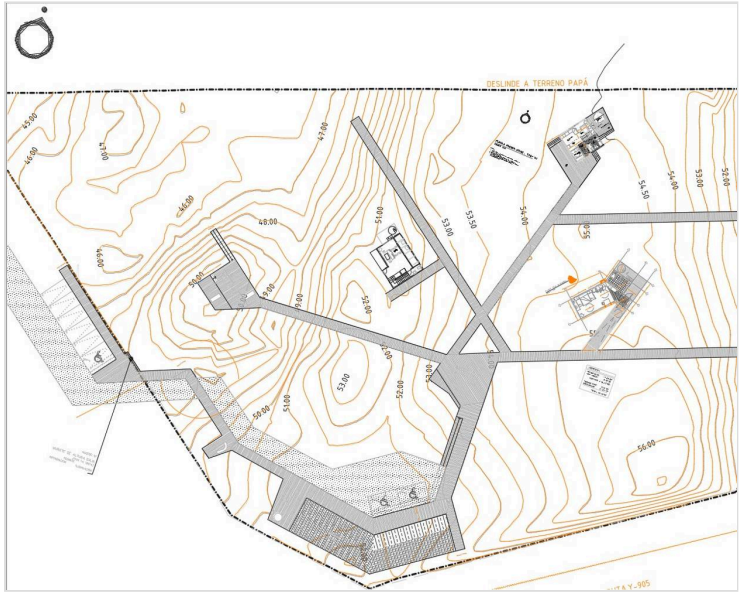



01


Tiny House Cluster — Site

Isla Navarino, Cape Horn

Schematic design for a group of small dwellings in the subantarctic forest. Buildings follow the contour lines and open paths between existing trees.

SITE SURVEY · MASTERPLAN



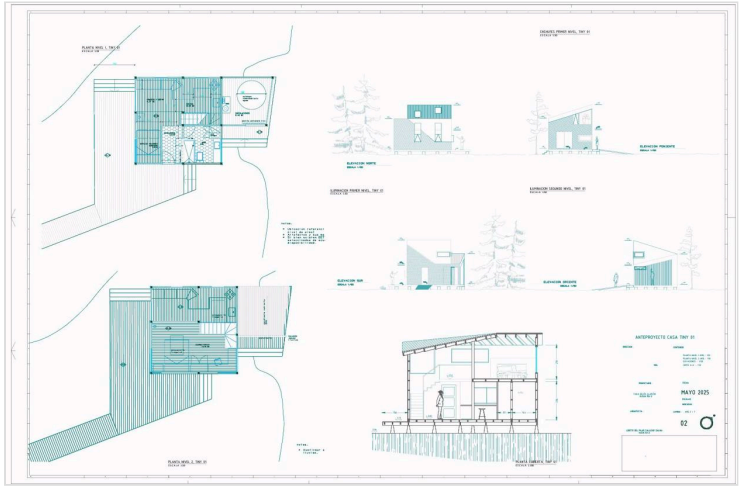




01


Tiny House Cluster — Unit A


Isla Navarino, Cape Horn


Compact timber unit with a single sloped roof and a covered deck, sized for an extreme climate and simple construction.

DESIGN · DRAWINGS · 3D MODEL

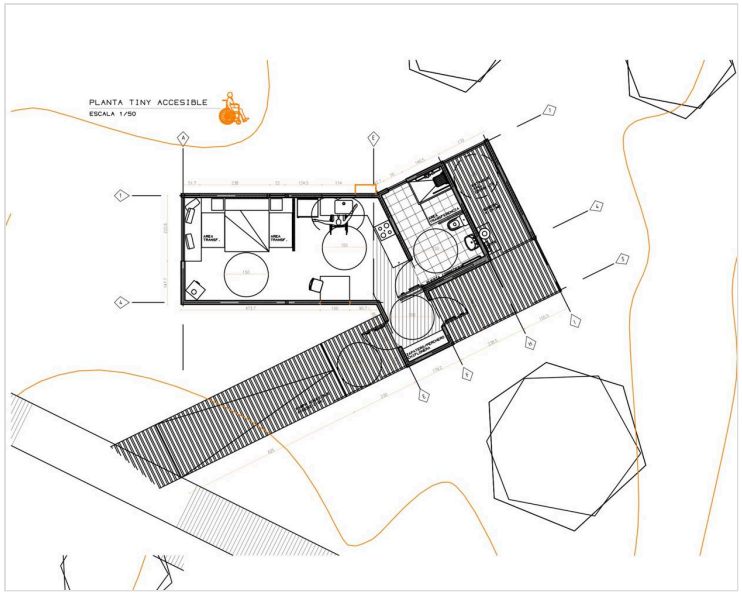

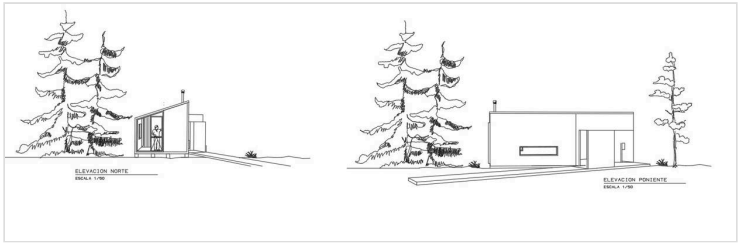

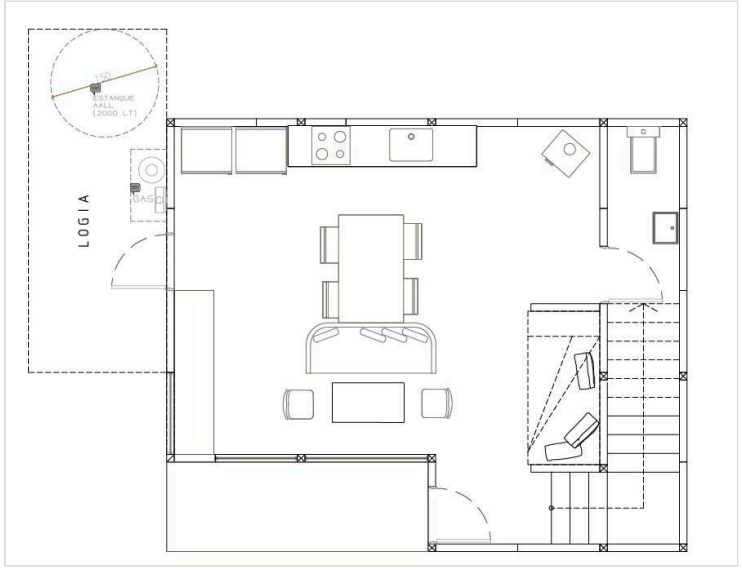

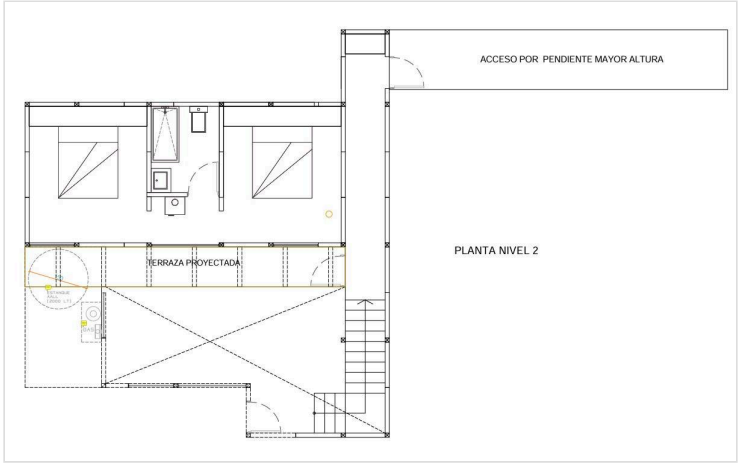

01

Tiny House Cluster — Accessible and Larger Units


Isla Navarino, Cape Horn

Unit B adapted for reduced mobility, and a two-level house for families, using the same timber system and roof language.

UNIVERSAL ACCESSIBILITY · DESIGN



Site · 3D terrain model, Manquemapu bay

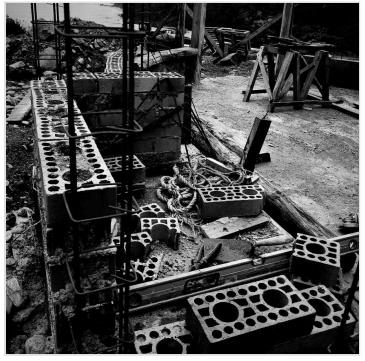







02

Refugio Leucotón

Mapu Lahual Biosphere Reserve · Manquemapu, Osorno, Los Lagos Region · 2025–2026

A gathering place for local culture on a remote stretch of the Chilean coast, with limited services: a fire hearth, food made with local products, kayaking and local crafts. Built with local craftsmen on strip foundations and a concrete slab, with cement-brick walls and native timber, to sit quietly in the landscape.


DESIGN · CONSTRUCTION · SITE SUPERVISION



Render



SketchUp model

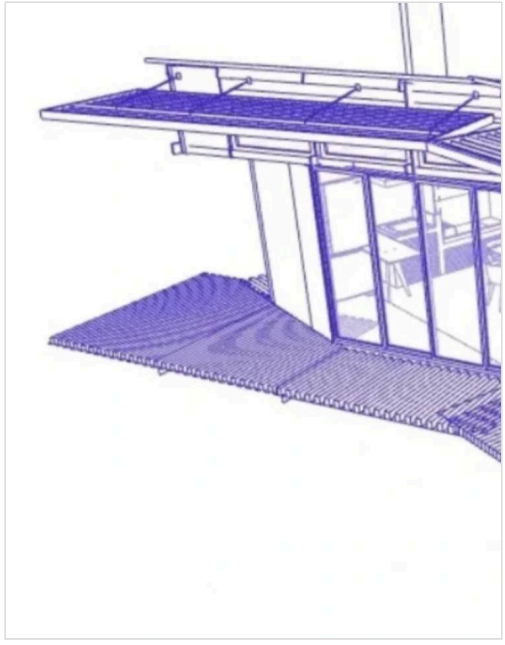

SketchUp model · structure

03

Quincho Pucón


Lote 32, Los Cipreses · Pucón, Araucanía · 2025–2026

Pavilion with kitchen, living area, office and bathroom on a 5,244 m² forested lot. A long glazed façade under deep timber eaves opens onto a continuous deck, keeping the existing trees.


DESIGN · 3D MODEL · VISUALIZATION




Site location

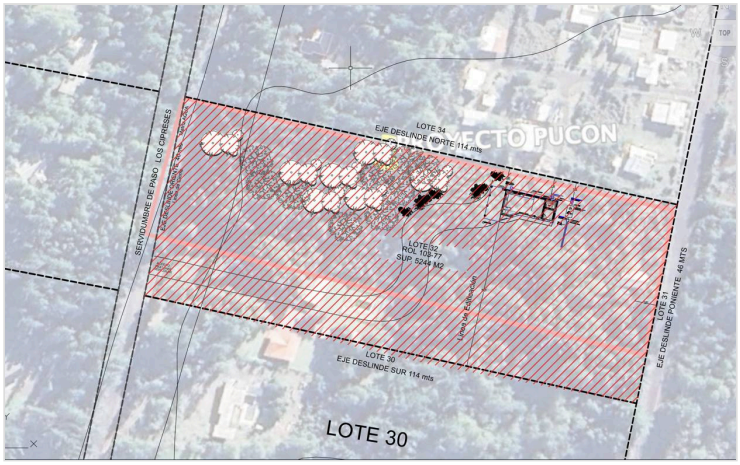

Site plan

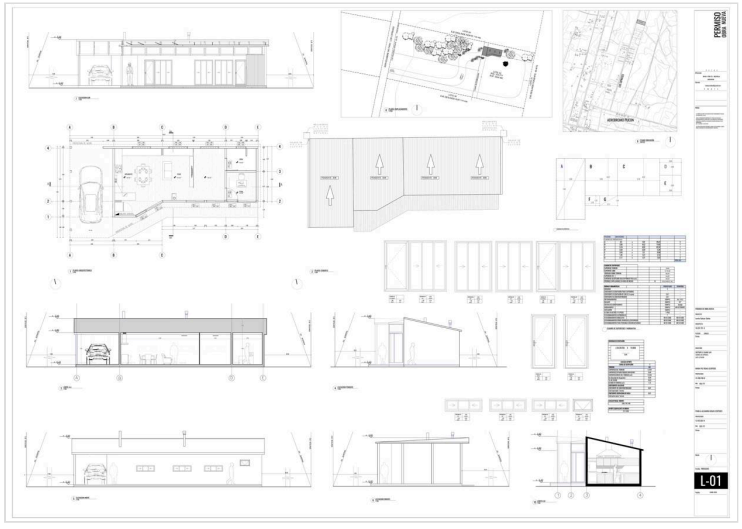

Permit sheet L-01

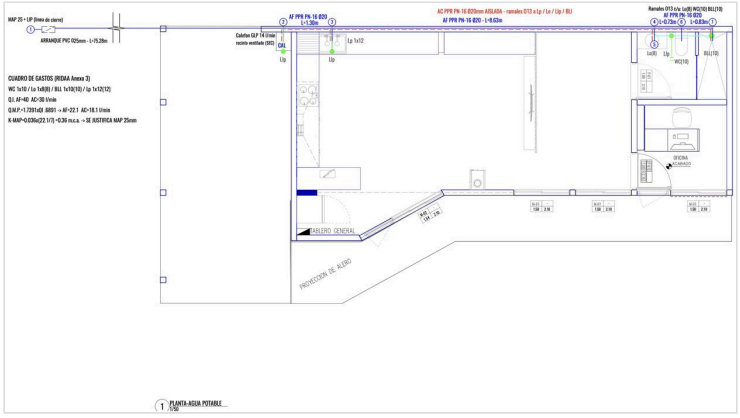

Drinking-water plan (RIDAA)


03

Quincho Pucón — Permit Set


Lote 32, Los Cipreses · Pucón, Araucanía

Full building-permit documentation: site analysis, site plan with building line and protected trees, architecture drawings, and drinking-water design calculated under Chilean RIDAA standards.


PERMIT DOCUMENTATION · AUTOCAD · WATER DESIGN

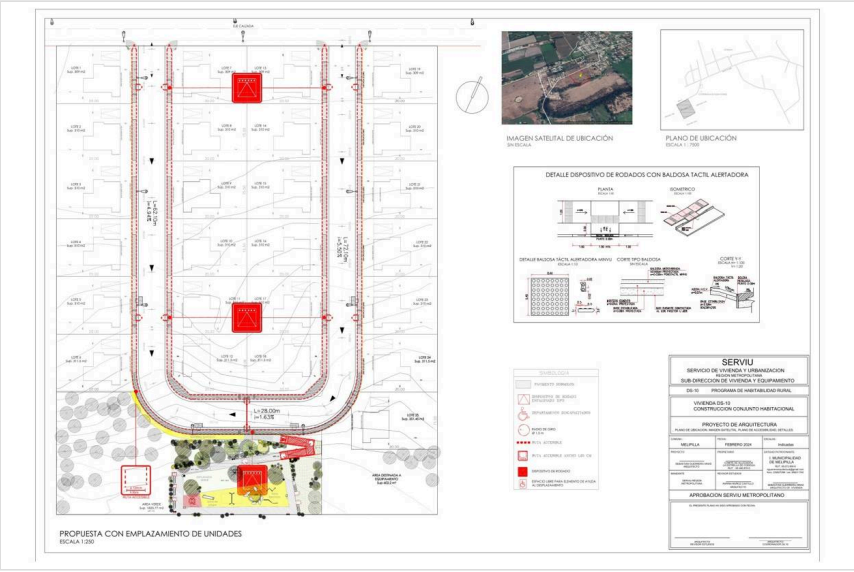

Site plan · accessible route and tactile paving details

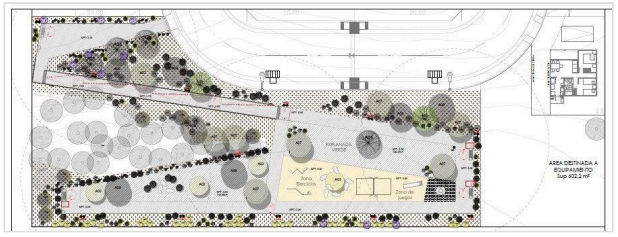

Green area with play and exercise zones

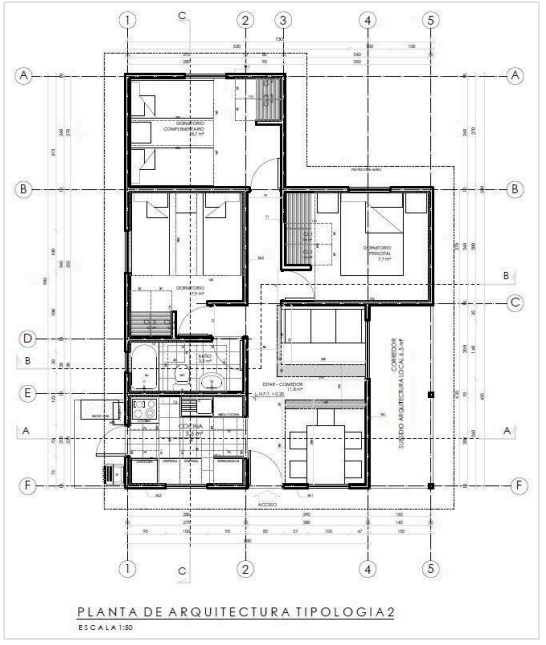

Housing typology 2 · 1:50


04

Social Housing Complex — Universal Accessibility

La Estrella de Codigua, Melipilla · 2024

Municipal housing office, D.S. 10 Rural Habitability Program: site plan for 25 subsidized homes with an accessible route, curb ramps with tactile paving, turning radii and green area, prepared for approval by SERVIU Metropolitano.


MUNICIPAL TEAM · ACCESSIBILITY PLAN · SOCIAL HOUSING

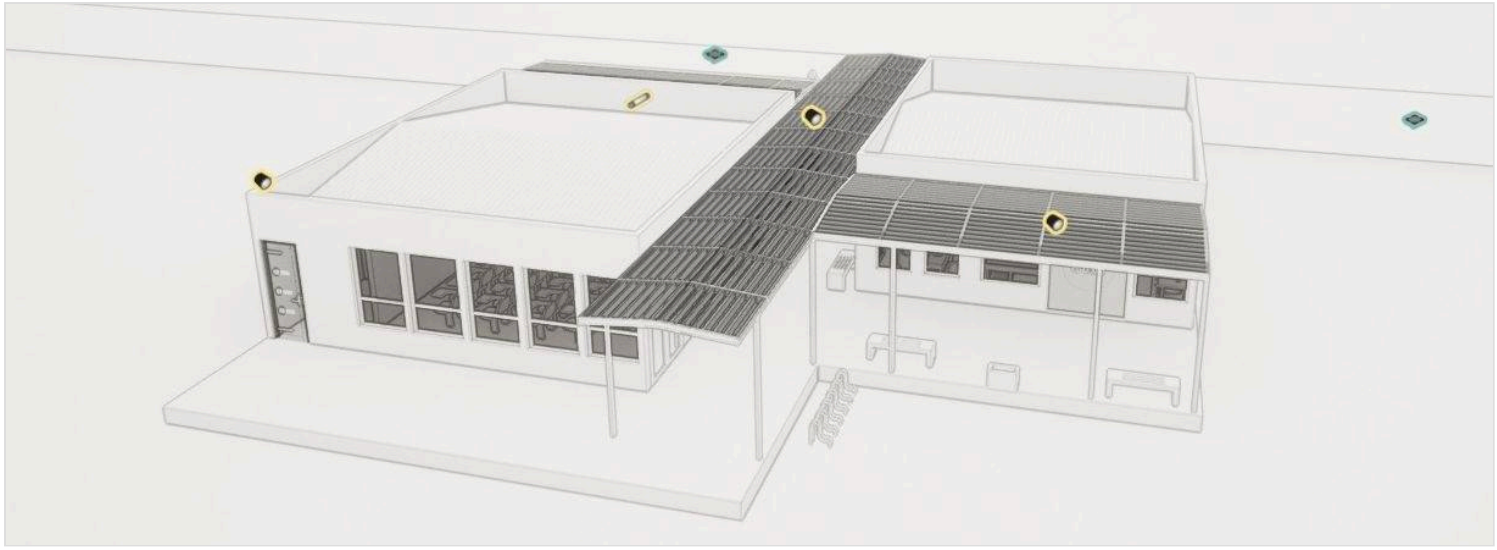

3D model



Covered walkway

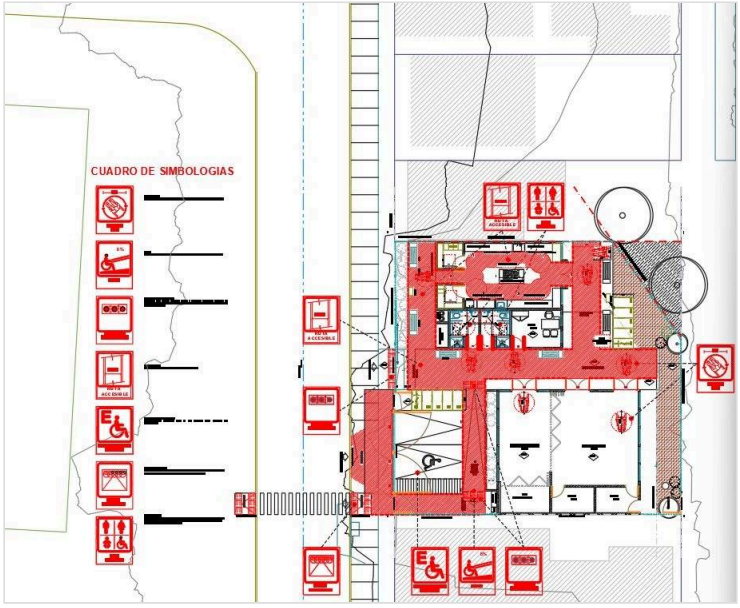

Universal accessibility plan


05

Community Center El Llano

Melipilla · Municipal project

Community center developed with the municipal team: two volumes linked by a covered walkway with a timber-slat roof, an accessible route through the whole building, universal-access restrooms and wayfinding signage.

MUNICIPAL TEAM · UNIVERSAL ACCESSIBILITY · 3D MODEL

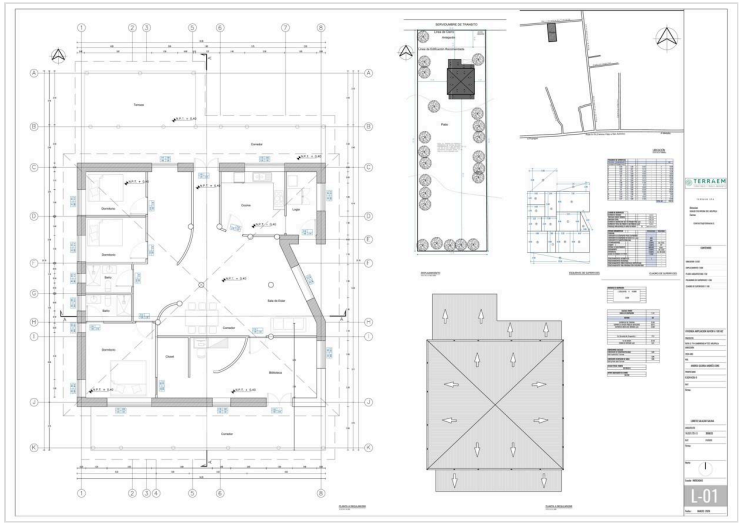




06

Adobe Dwelling Regularization

Lumbreras, Melipilla · 2026

Survey and permit documentation of an existing adobe house in a rural area, recording the original building to bring it into compliance while keeping its character.

SURVEY · DRAWINGS · PERMIT

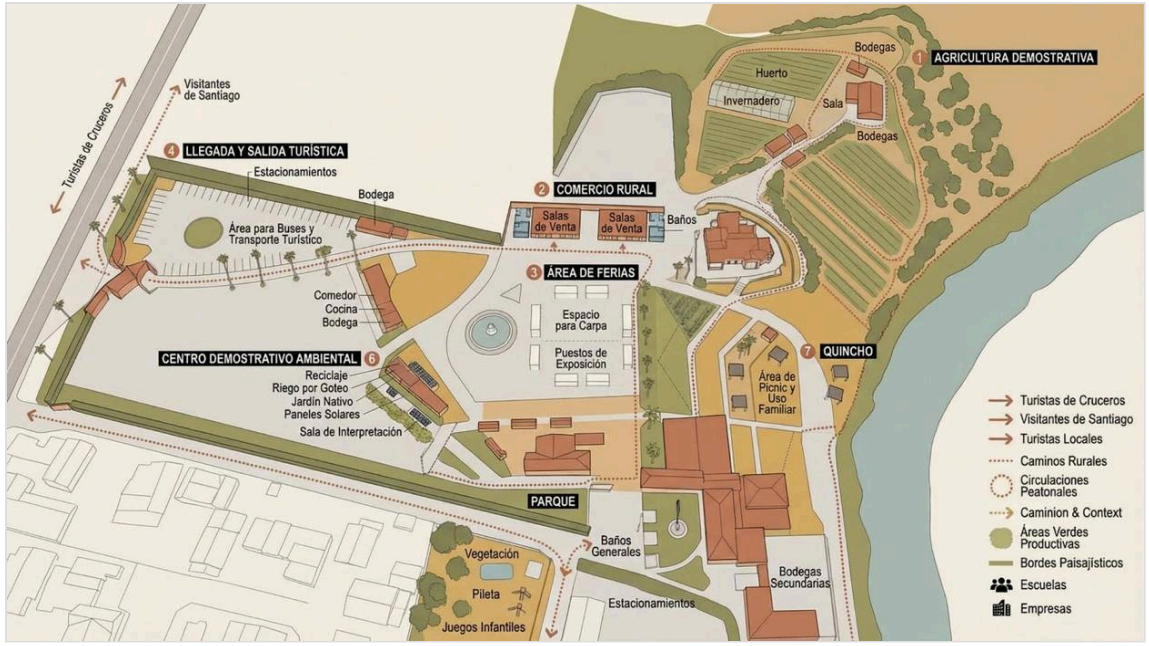




07


Rural Tourism Masterplan

Altos de Culiprán, Melipilla

Agri-tourism park with arrival and bus area, rural market, fair plaza, demonstration farming, environmental center and picnic areas, organized along rural paths and landscape edges.

MASTERPLAN · TERRITORIAL PLANNING

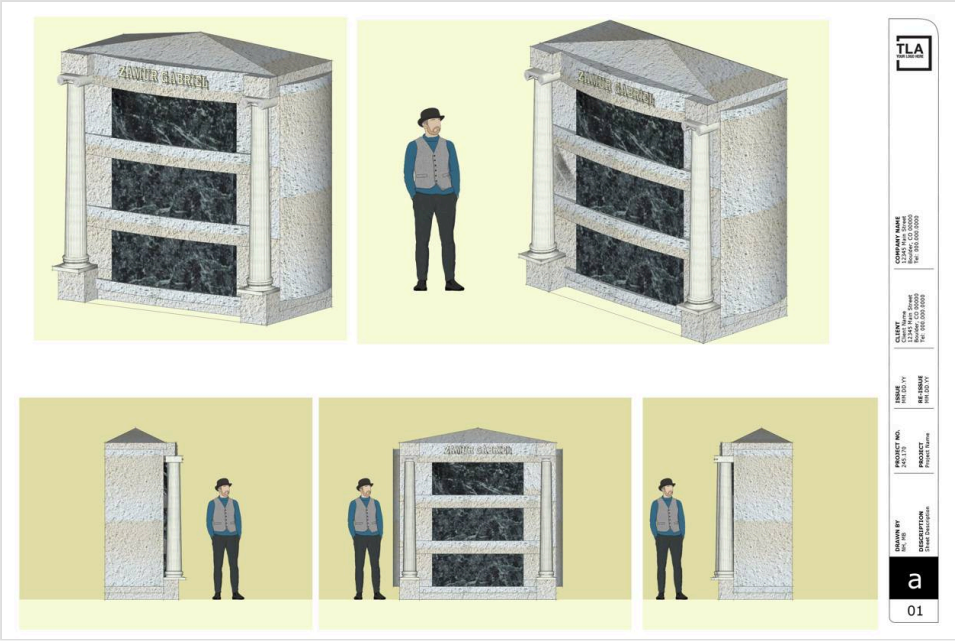

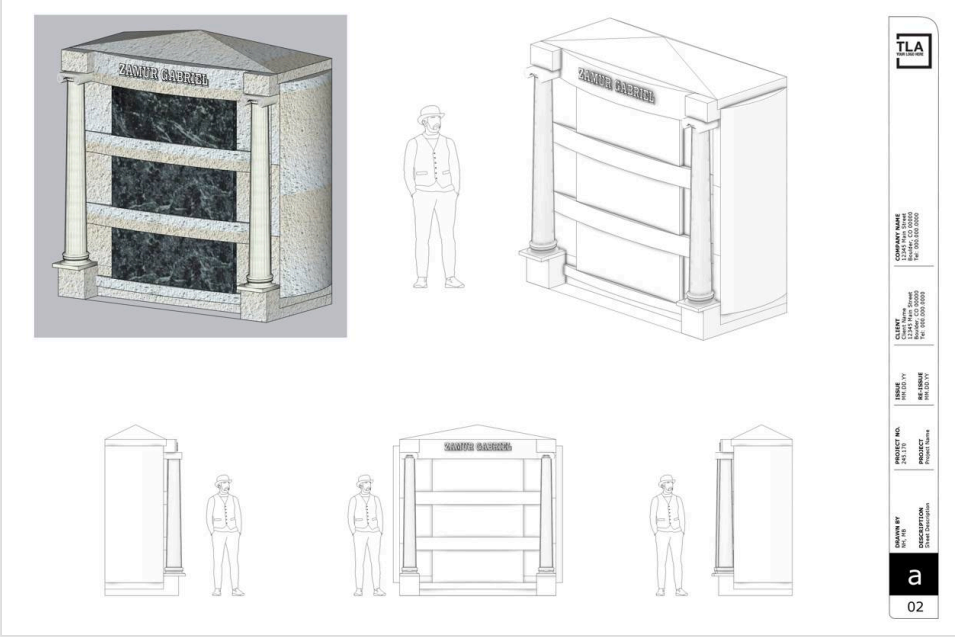


08

Family Mausoleum

Municipal Cemetery, Melipilla · 2026

Vertical family tomb built around heritage Ionic columns rescued from the former Arab Center of Melipilla. Mixed confined masonry and reinforced concrete system.

DESIGN · 3D MODEL · TECHNICAL DETAILS

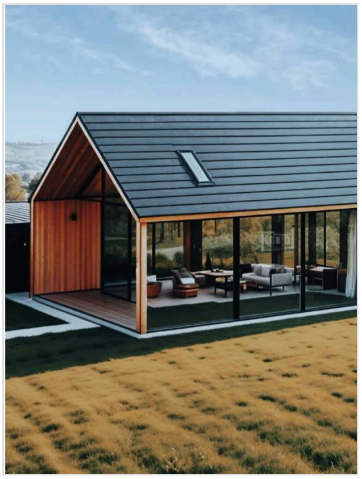






09


3D Studies — Timber Cabins


Own practice · 2024–2026


A series of small timber cabins and refuges explored in 3D: gable and mono-pitch roofs, deep porches, dark and natural cladding, and large openings toward the forest.


3D MODELING · VISUALIZATION

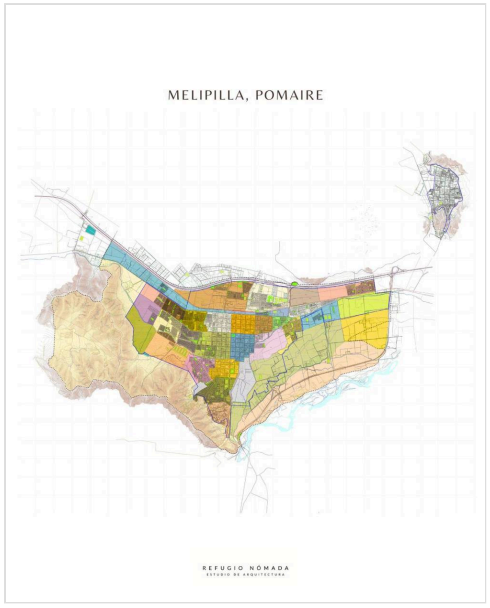


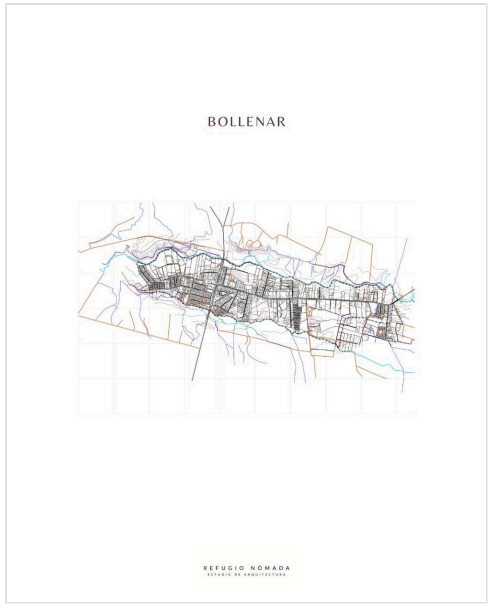

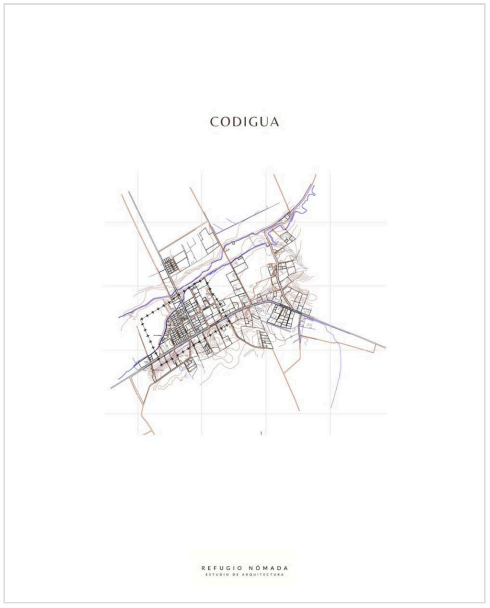

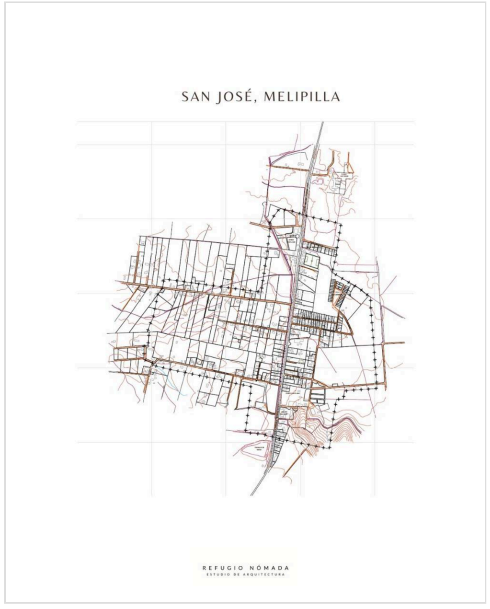

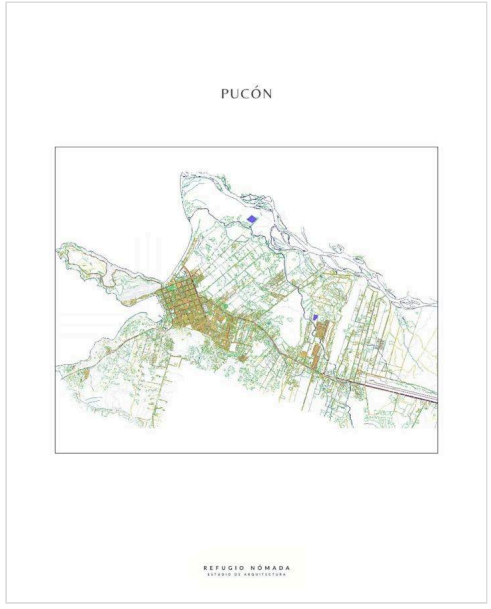

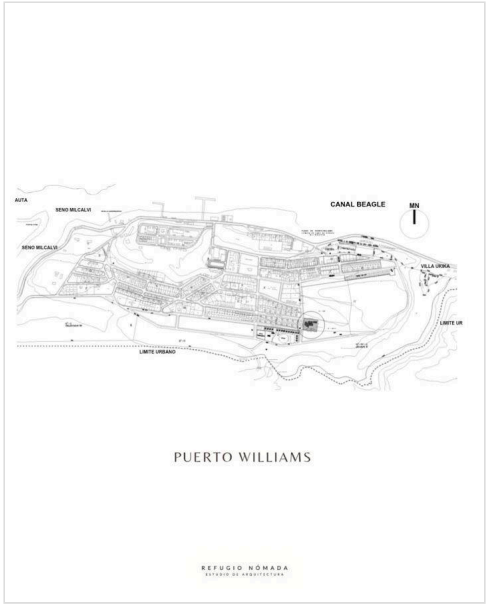

10

Territorial Readings

Melipilla, Pomaire, Bollenar, Codigua, San José, Pucón, Puerto Williams

Every project starts by reading the territory: roads, water, settlement patterns and landscape. These maps are part of my own analysis before design.

TERRITORIAL ANALYSIS · MAPPING

Thank you

Loreto Salazar Salina
Architect · Chile · Reg. N° 300833

lsalazarsalina@gmail.com
+56 9 7952 5044 (WhatsApp)
refugionomada.cl (EN/ES)
Instagram @lsalazarsalina

